



Legenda :

- : 2 Hole (1 Pasang) Stop Kontak Jaringan
- : 12 Hole (6 Pasang) Stop Kontak Jaringan

Keterangan

- Setiap Ruang Terhubung 2 Line Jaringan Ke Ruang Server
- Ruang Pengendali (belum Tergambar) Terhubung 2 Line Jaringan Ke ruang server
- Tinggi Wall Plate adalah 75cm , kecuali di Koridor luar 3 M untuk Wifi acces Point

PROJECT TTT
Denah Stop Kontak Jaringan
(Network Wall Plate)
Rev 1 2




Legenda :

☒ : 1 Hole Stop Kontak Listrik

Keterangan

- Tinggi Jalur Stop Kontak adalah 70 CM di ruang Siswa dan Pengendali
- Di Koridor dan Luar ada Stop kontak tinggi 3 m untuk Access Point
- Kebutuhan Listrik ruang Siswa adalah 12 Ampere (3500 Watt)
- Kebutuhan Listrik ruang Pengendali adalah 20 Ampere (4400 Watt)
- Kebutuhan Listrik Ruang server adalah 30 Ampere (6600 Watt)

PROJECT TTT
Denah Stop kontak Listrik
 Rev 1 2

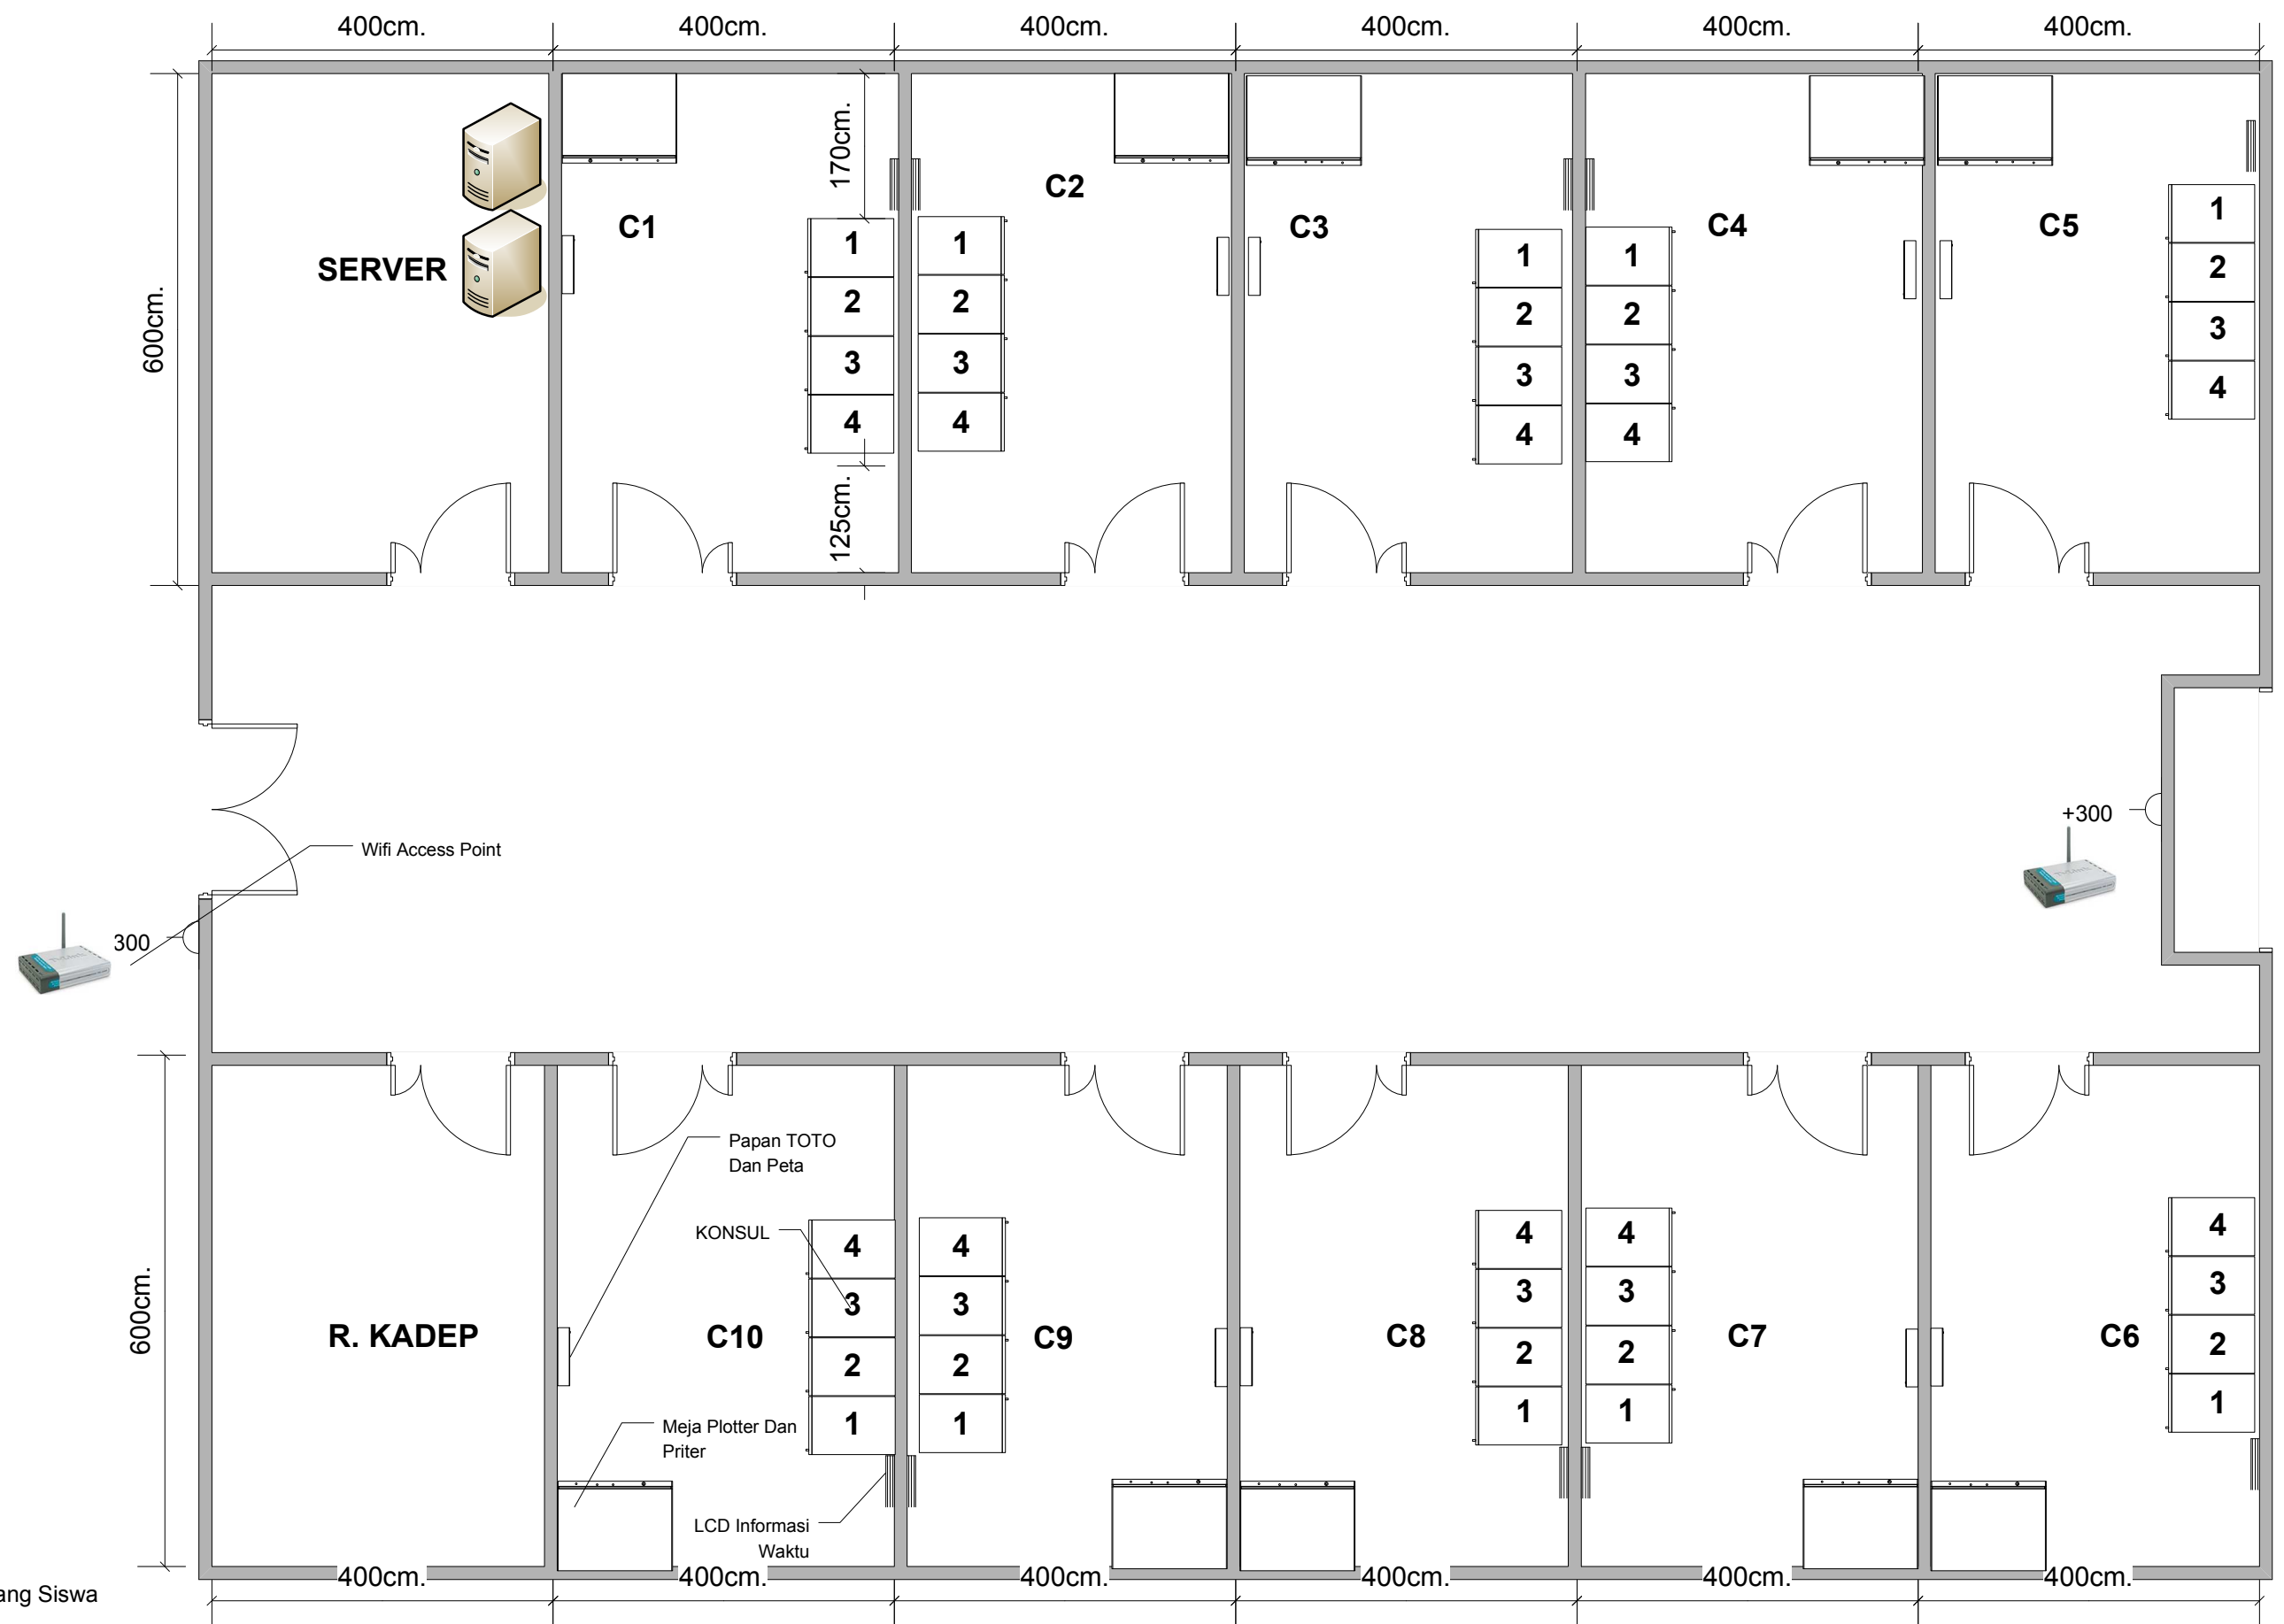

Peralatan Dalam Ruang Siswa

1. 4 Konsul Siswa
2. 1 Meja Plotter
3. 1 Pasang Papan TOTO
4. LCD Informasi Waktu
5. Printer
6. AC
7. Dehumidifier

Peralatan Dalam Ruang Pengendali (Belum Tergambar)

1. 4 Konsul Instruktur
2. 1 CCTV Server
3. LCD Informasi Waktu
4. Printer
5. AC
6. Dehumidifier

PROJECT TTT
Denah Peletakan Alat

PROJECT DPMS
Denah Listrik dan Data

DIAGRAM LISTRIK

Keterangan Listrik

- 1. Kebutuhan Daya Listrik untuk 1 ruang DPMS adalah 50A (Belum Termasuk AC)
- 2. Daya Utama ada di 4 x 2 stop kontak
- 2. Stop Kontak Dengan Tinggi +250 digunakan utk AC
- 3. Peletakan AC di ruang Instruktur Bisa dirubah
- 4. Aplikasi Stop Kontak Di Ruang Siswa Lain mengikuti ruang 1

Legenda :

-  : 1 hole Stop Kontak (Wall Plate) Jaringan
-  : 4 Hole Stop Kontak Jaringan
-  : 1 Hole, Stop kontak Listrik



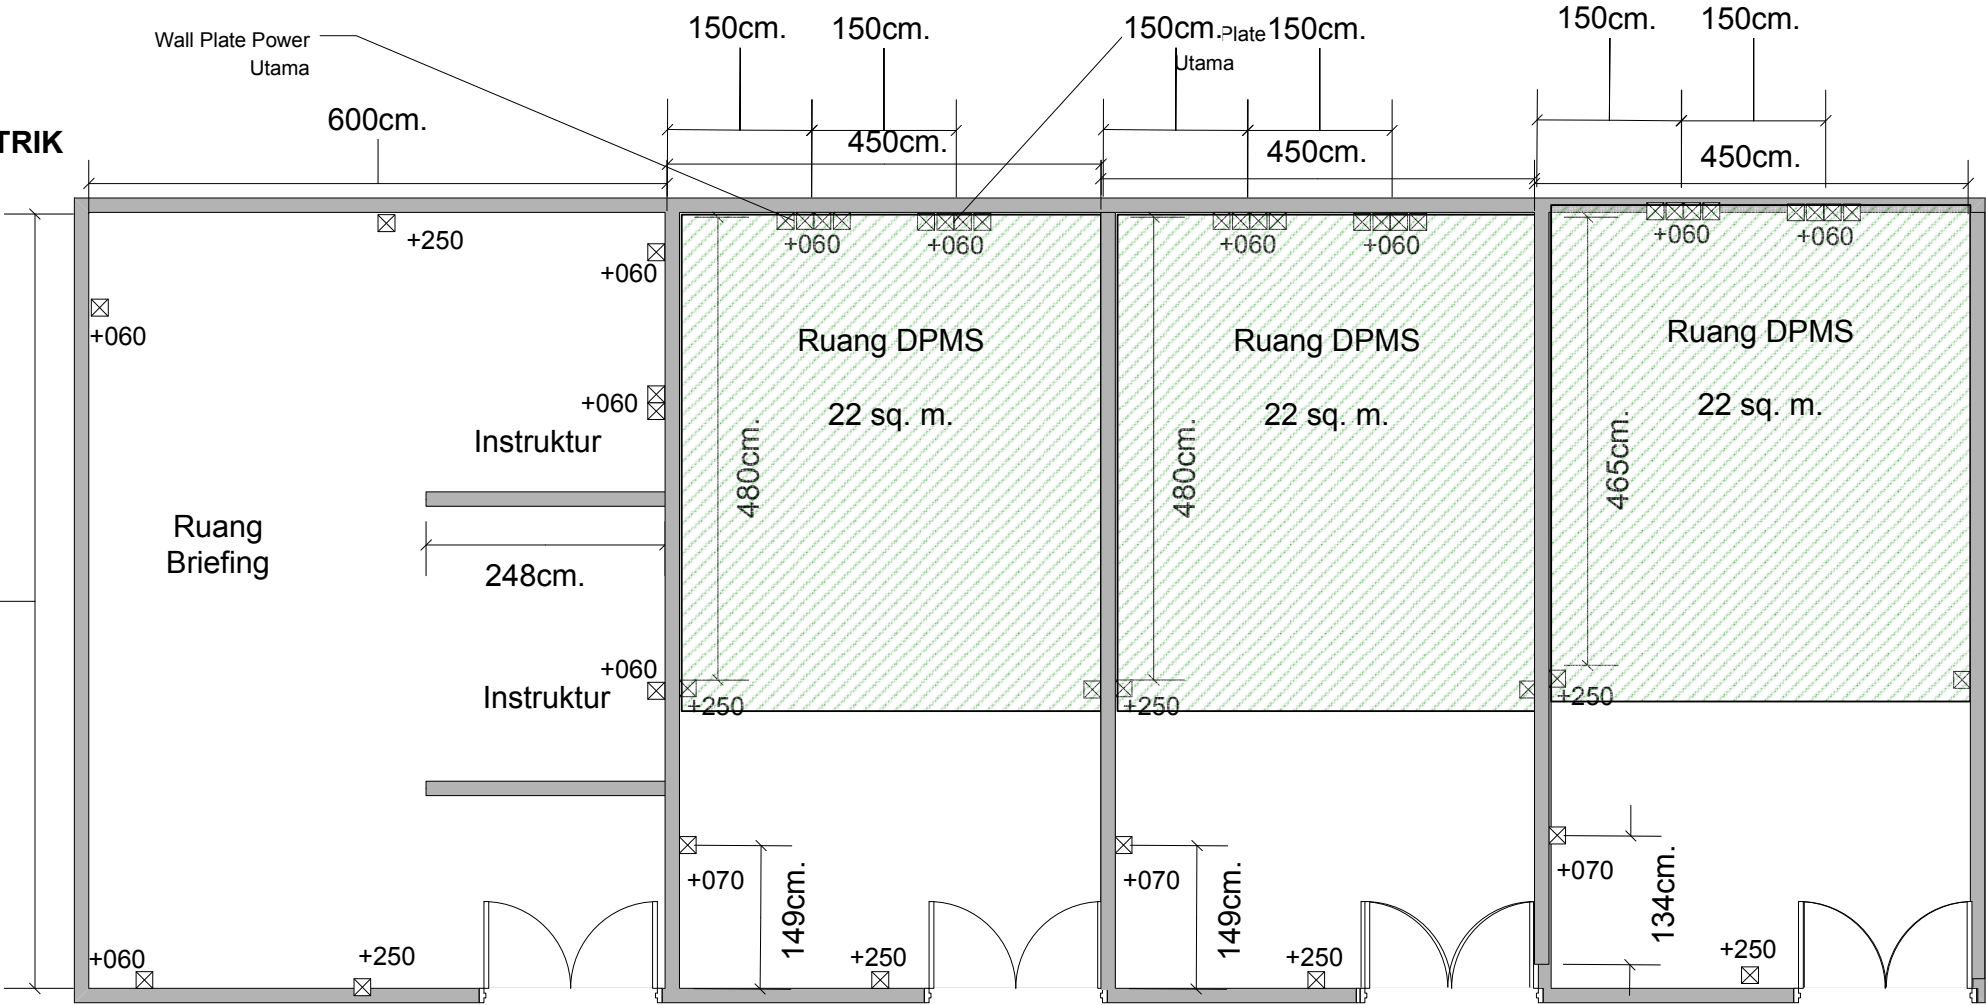


DIAGRAM JARINGAN DATA

Keterangan Jaringan Data

- 1. Stop kontak Jaringan Terhubung ke Server
- 2. Adanya Cable Ducting setinggi 30 Cm , untuk 20 Nework Cable Yang menembus tembok dari Server sampai cubicle 3

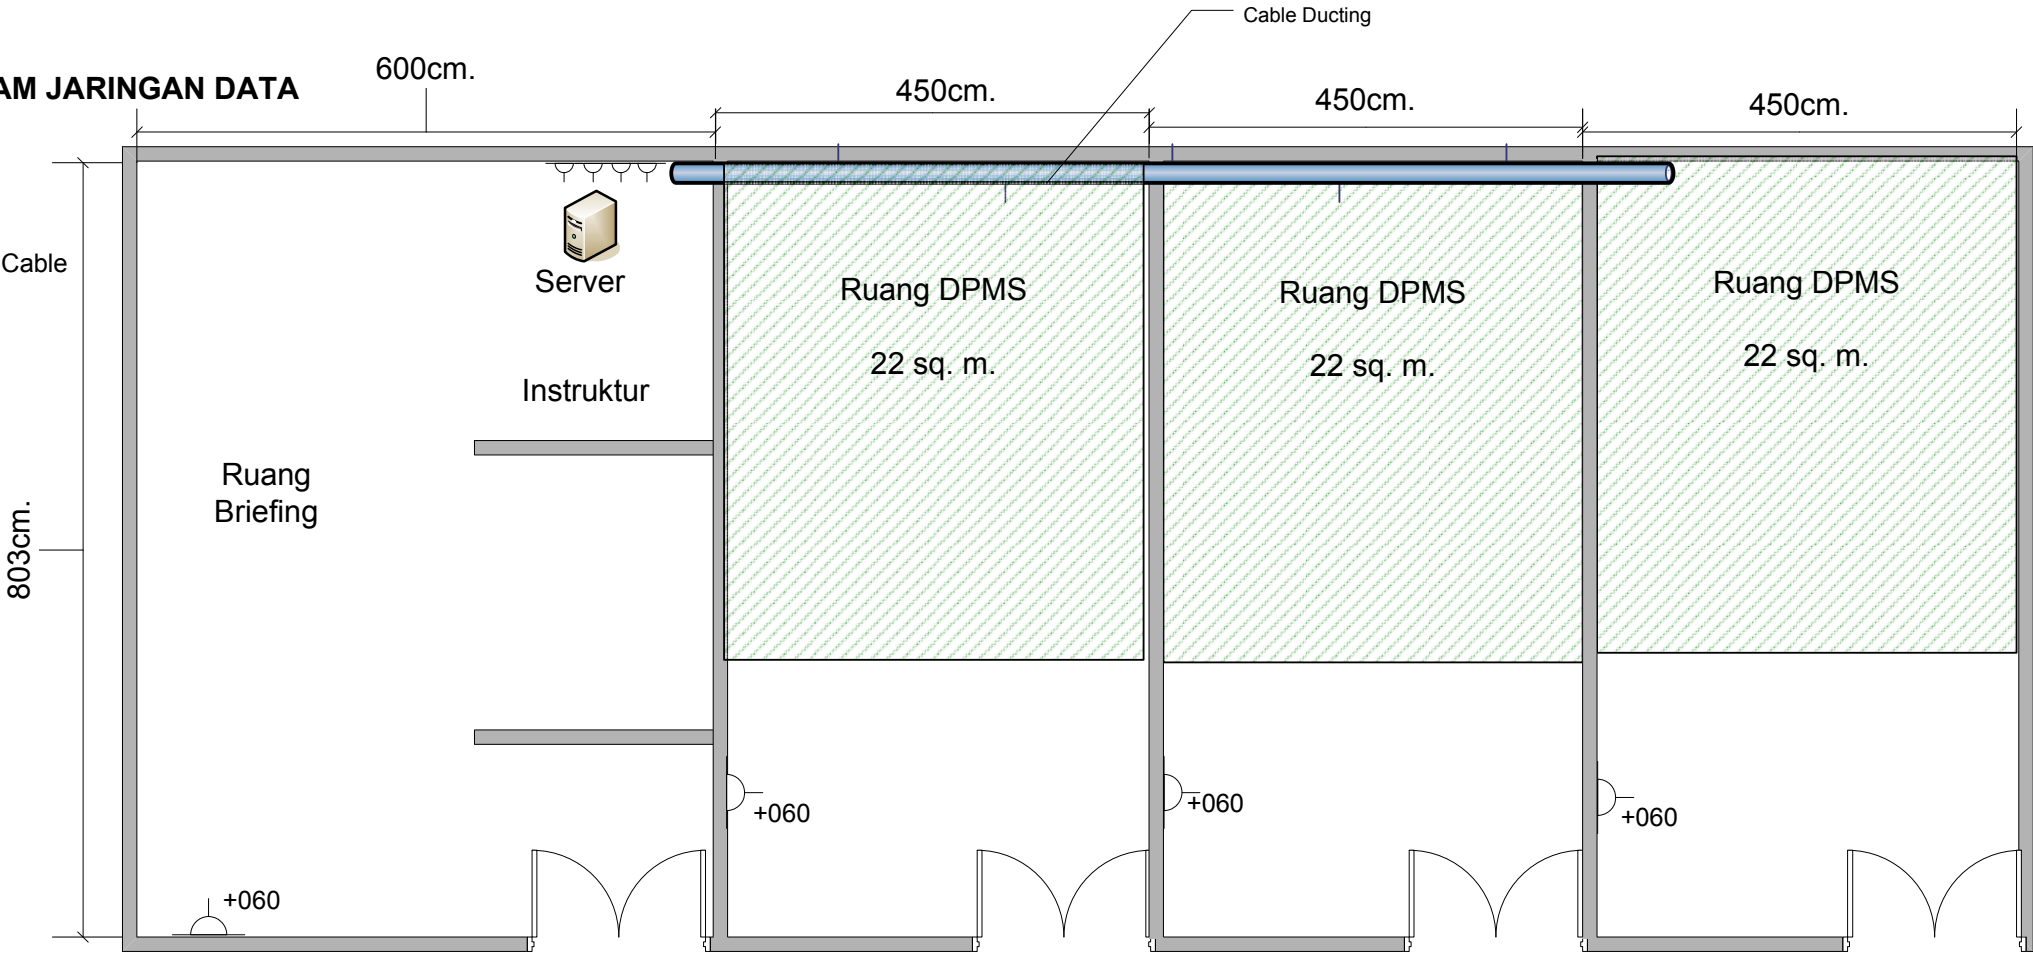

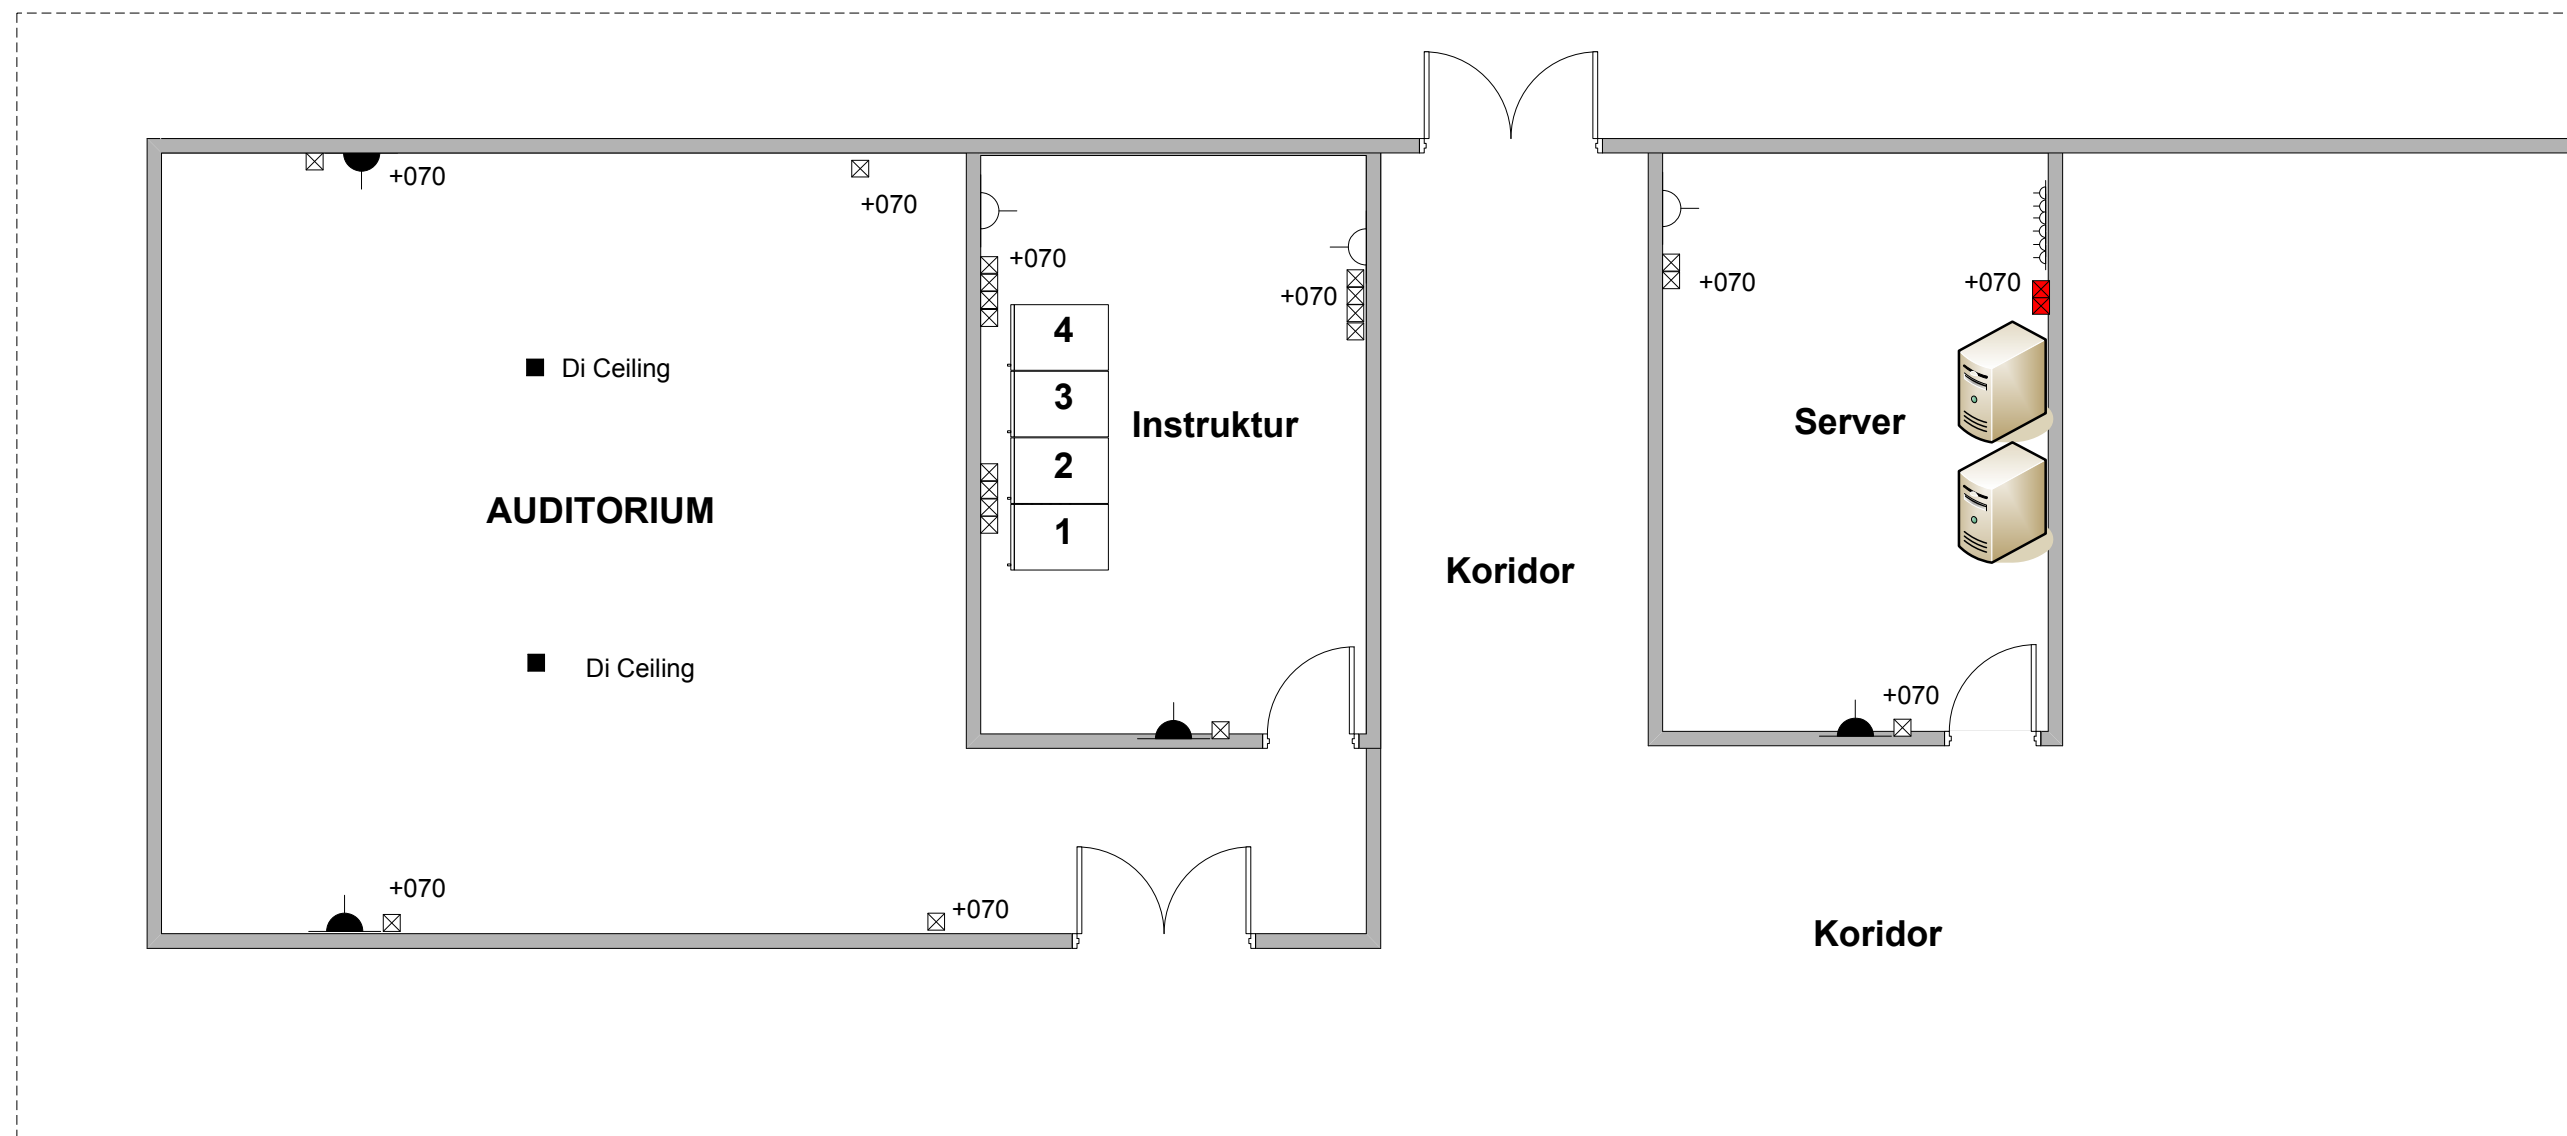

Legenda :

-  : 2 Hole (1 Pasang) Stop Kontak Jaringan
-  : 1 Stop Kontak Jaringan
-  : 1 Hole Stop Kontak Listrik
-  : 1 Hole Stop Kontak Listrik Dengan total daya (4400 watt) 20 A

Keterangan

- Ruang Instruktur ada 5 line jaringan yang terhubung ke server
- Ruang Auditorium ada 2 line jaringan ke server
- Daya Listrik Ruang Instruktur adalah 4400 watt (20A)
- **Daya Listrik di Ruang Server adalah 6600 Watt (30 A) , (Bukan 4400)**
- Di ruang server kabel dibiarkan terurai dengan cadangan 2,5 Meter
- Tinggi Wall Plate adalah 75cm , kecuali di Koridor luar 3 M untuk Wifi acces Point

PROJECT TTT
Power Line dan Jaringan R. Instruktur
 Ver 1 1